


Skyline - variante 2 : vue d'ensemble (couche A beige = fond, couche B grise = devant). Fenetres = decoupes (ambre/rouge).

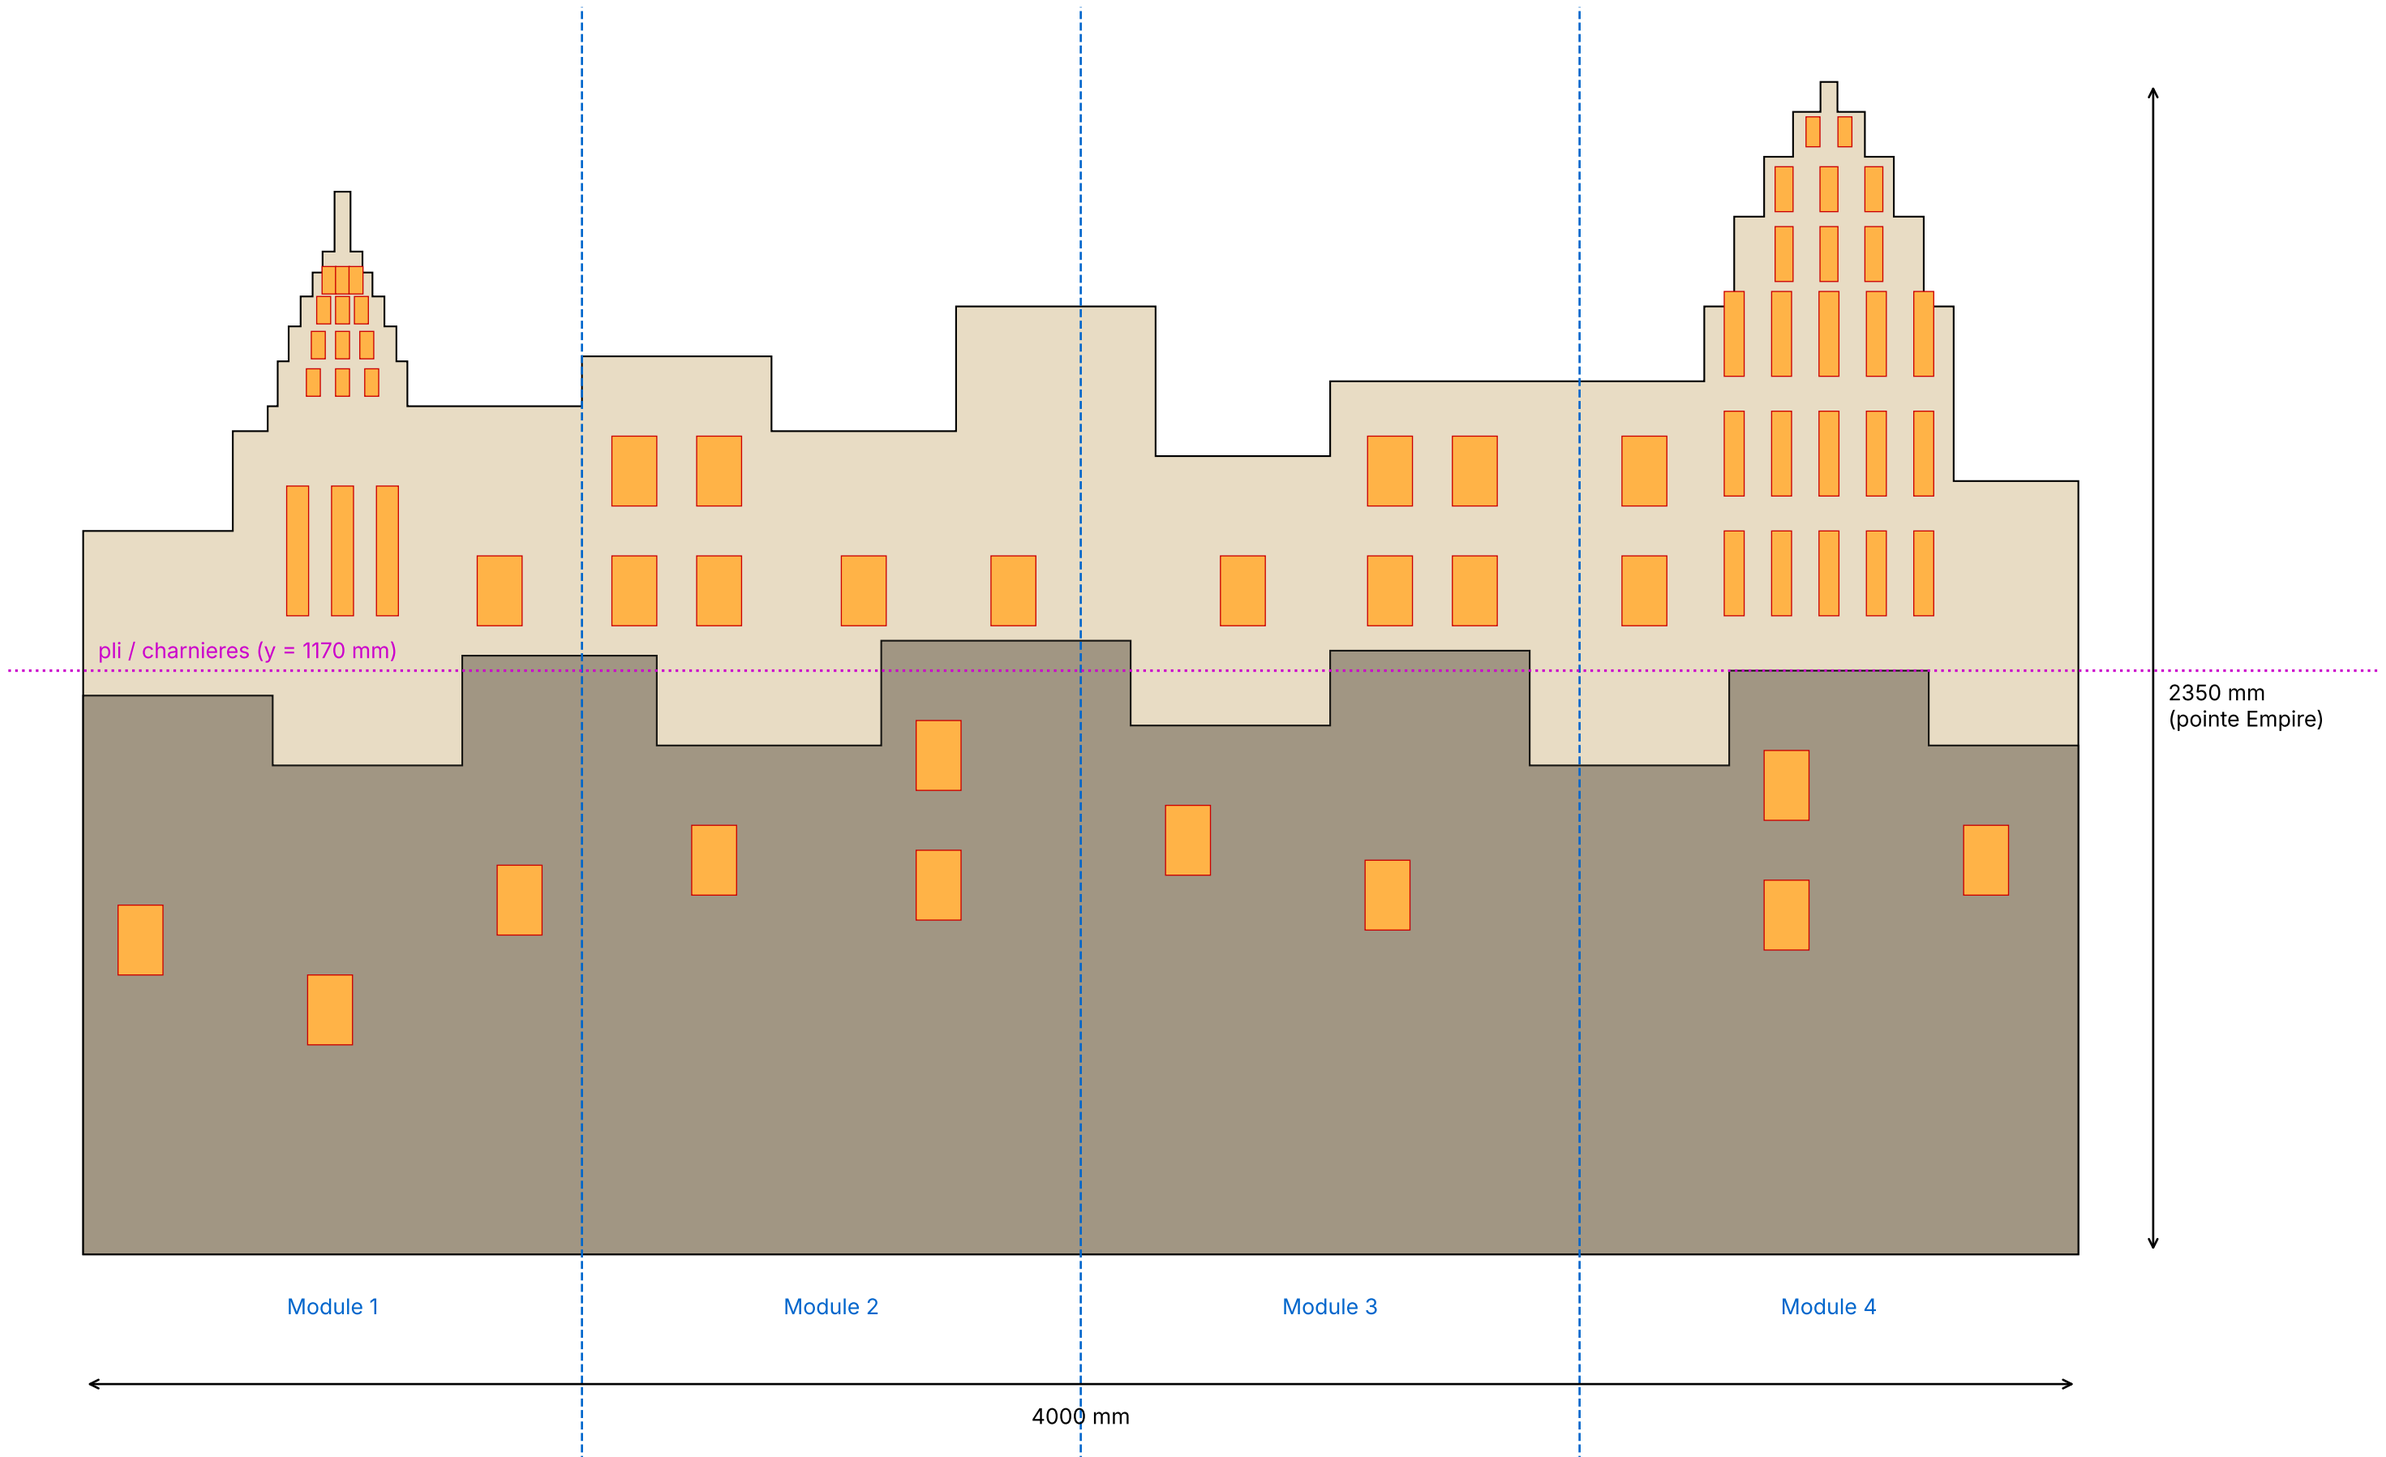

Couche A : 4 modules de 1000 mm (a decouper dans des panneaux 1220 × 2440 mm, contreplaque 10 mm)

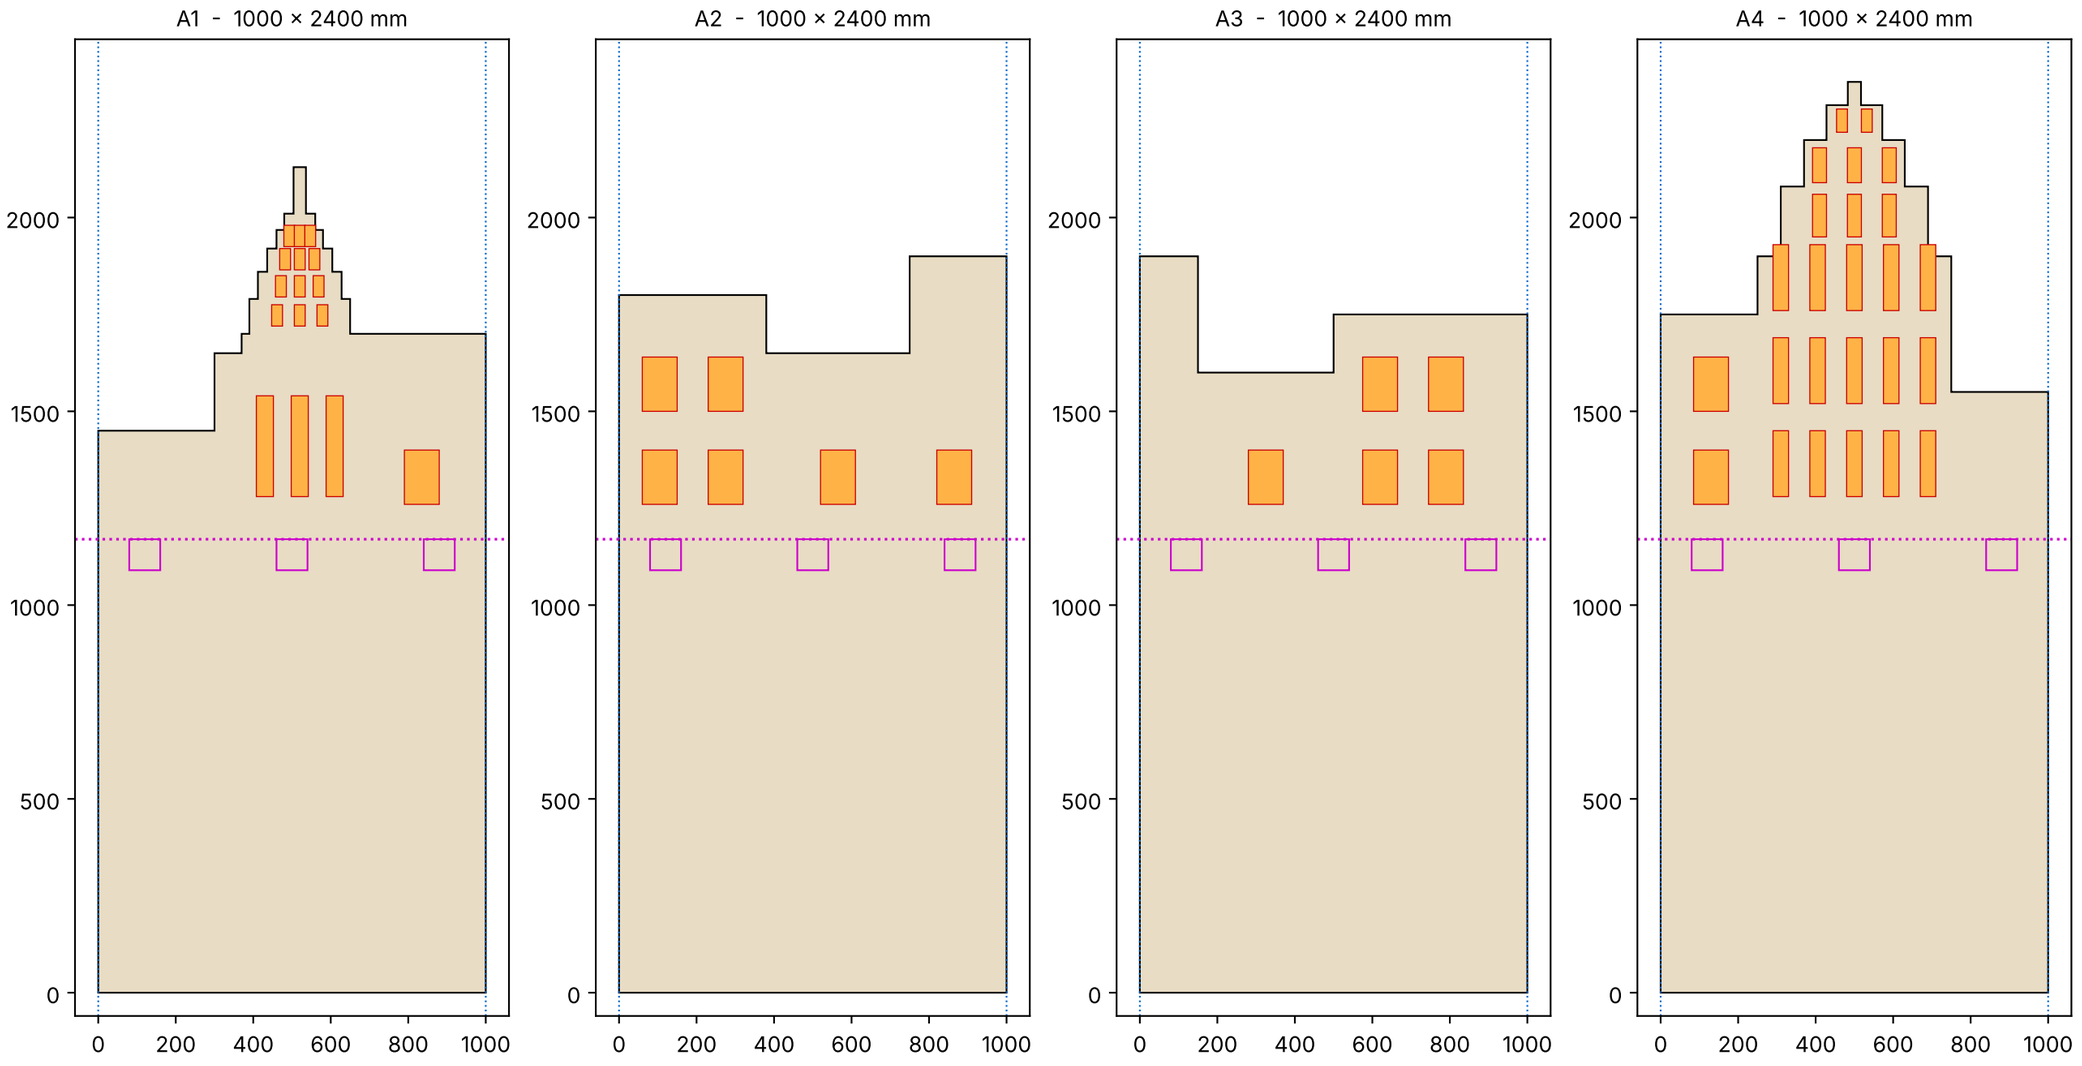

Couche B : 4 modules de 1000 mm (a decouper dans des panneaux 1220 × 2440 mm, contreplaque 10 mm)

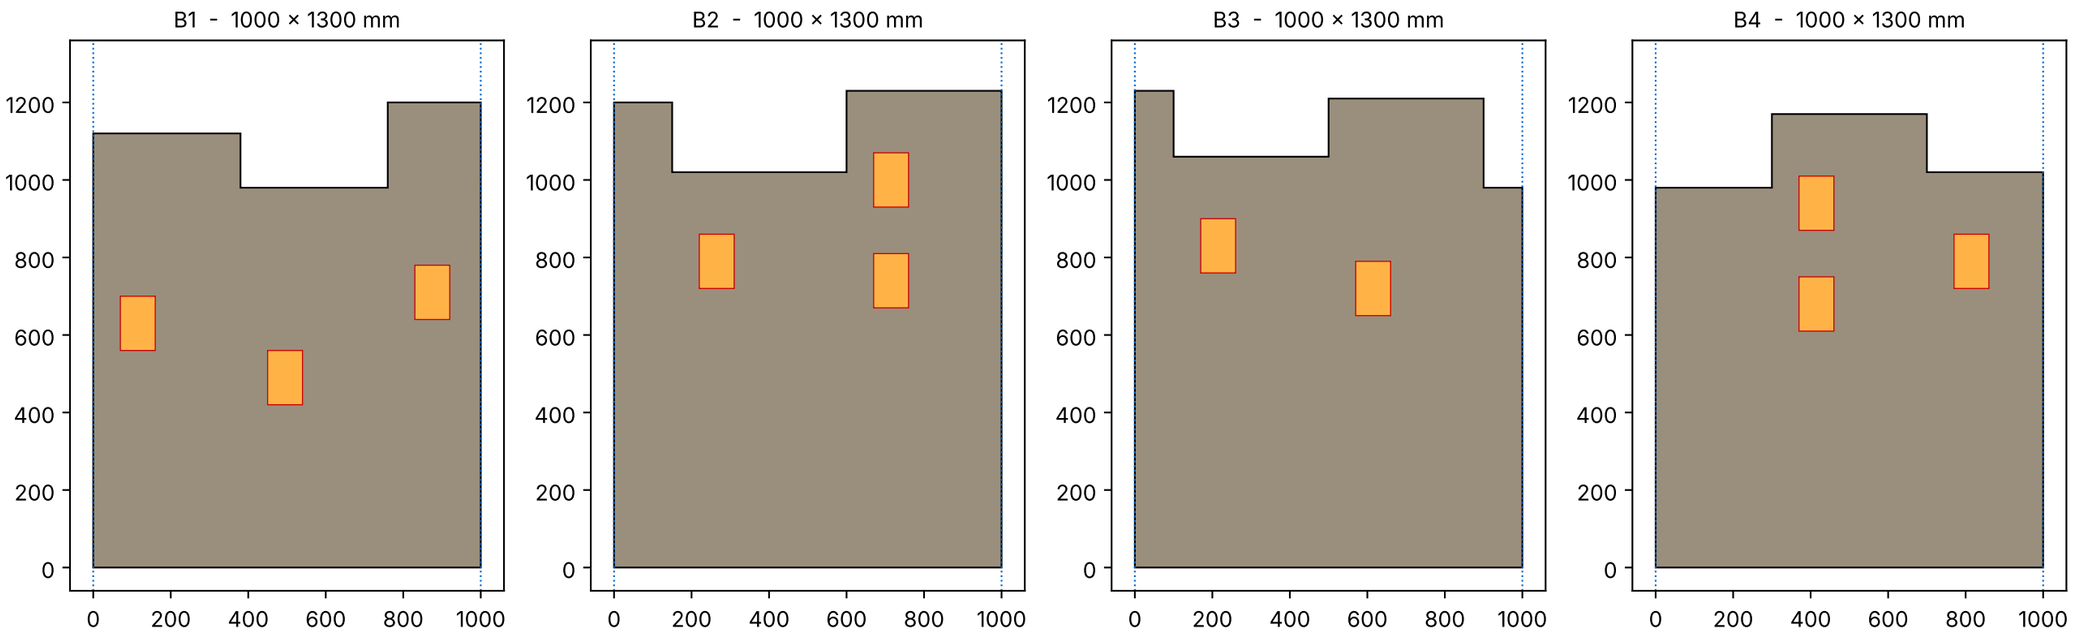

Notes de fabrication - variante 2

Dimensions : largeur 4000 mm, hauteur maximale 2350 mm (pointe de l'Empire State).
Decoupe en 4 modules de 1000 mm. Chaque module tient dans un panneau de contreplaque 1220 x 2440 mm (couche A) ou, par deux, dans un panneau (couche B, 1000 x 1300 mm).
Les tours (Chrysler a x=520 mm, Empire State a x=3500 mm) ne traversent aucun joint : aucun module ne coupe une fenetre ni une pointe.

Materiau : contreplaque 10 mm minimum (12 mm conseille pour les pointes), peint en noir mat. Tranche des immeubles : laisser le bois ou la peindre clair.
Quantite : couche A = 4 panneaux 1220 x 2440 ; couche B = 2 panneaux (2 modules par panneau). Soit 6 panneaux en tout.
Fenetres : 52 decoupes en couche A, 11 en couche B. Grandes fenetres 90 x 140 mm. Rayon d'angle 3 mm si decoupe a la defonceuse.
Pointes : largeur minimale 30 mm en haut. Renforcer par un tasseau colle derriere, sur 300 mm minimum sous la pointe.
Entre deux decoupes, garder au moins 40 mm de matiere.

Pliage (transport) : chaque module de la couche A est coupe en deux pieces au niveau y = 1170 mm, reliees par 3 charnieres (80 mm, repere en magenta) posees AU DOS. Replie, un module fait 1000 x 1170 mm, environ 30 mm d'epaisseur : il rentre dans un break ou un utilitaire et se porte seul.
 - Plier dos contre dos : les faces restent a l'exterieur, prevoir une housse ou des protections de coin.
 - Ouvert, verrouiller le pli avec un tasseau de 80 x 20 mm visse au dos ou 2 loquets : sans cela le module plie sous son poids.
 - Aucune fenetre ni pointe ne traverse le pli (la premiere fenetre est a 1260 mm).
 - Chaque module (1000 x 2350 mm au total) reste dans un seul panneau 1220 x 2440 : pieces superposees (1170 + 1180 mm).
 - La couche B (1000 x 1300 mm) se replie pas, elle est deja compacte.

Assemblage : relier les modules au dos par une latte de 80 x 20 mm vissee a cheval sur chaque joint (a 600 mm du sol et a 1800 mm).
Pieds : une equerre ou un pied en T a l'arriere de chaque module, lestes. Couche B posee 150 mm devant la couche A.
Eclairage : bandeau LED blanc chaud dans un caisson noir derriere chaque couche, vers la fenetre, avec un film diffuseur (calque epais ou film de diffusion) colle derriere les decoupes. LED uniquement, pas d'ampoule a filament.
Securite : demander aux salles si le bois doit etre traite contre le feu (classement M1 ou B-s1,d0 selon les lieux).

Ce plan est un dessin de principe fait a partir du rendu choisi, pas un plan valide par un menuisier. Verifier les cotes, l'epaisseur et la tenue des pointes avant de couper.
Formats fournis : PDF (lecture), SVG (echelle 1:1 en mm), DXF (decoupe numerique : A bas / A haut par module, puis B).